


3 METER FLOATING RECOVERY LINE
SPLICED TO LIFTING BALE

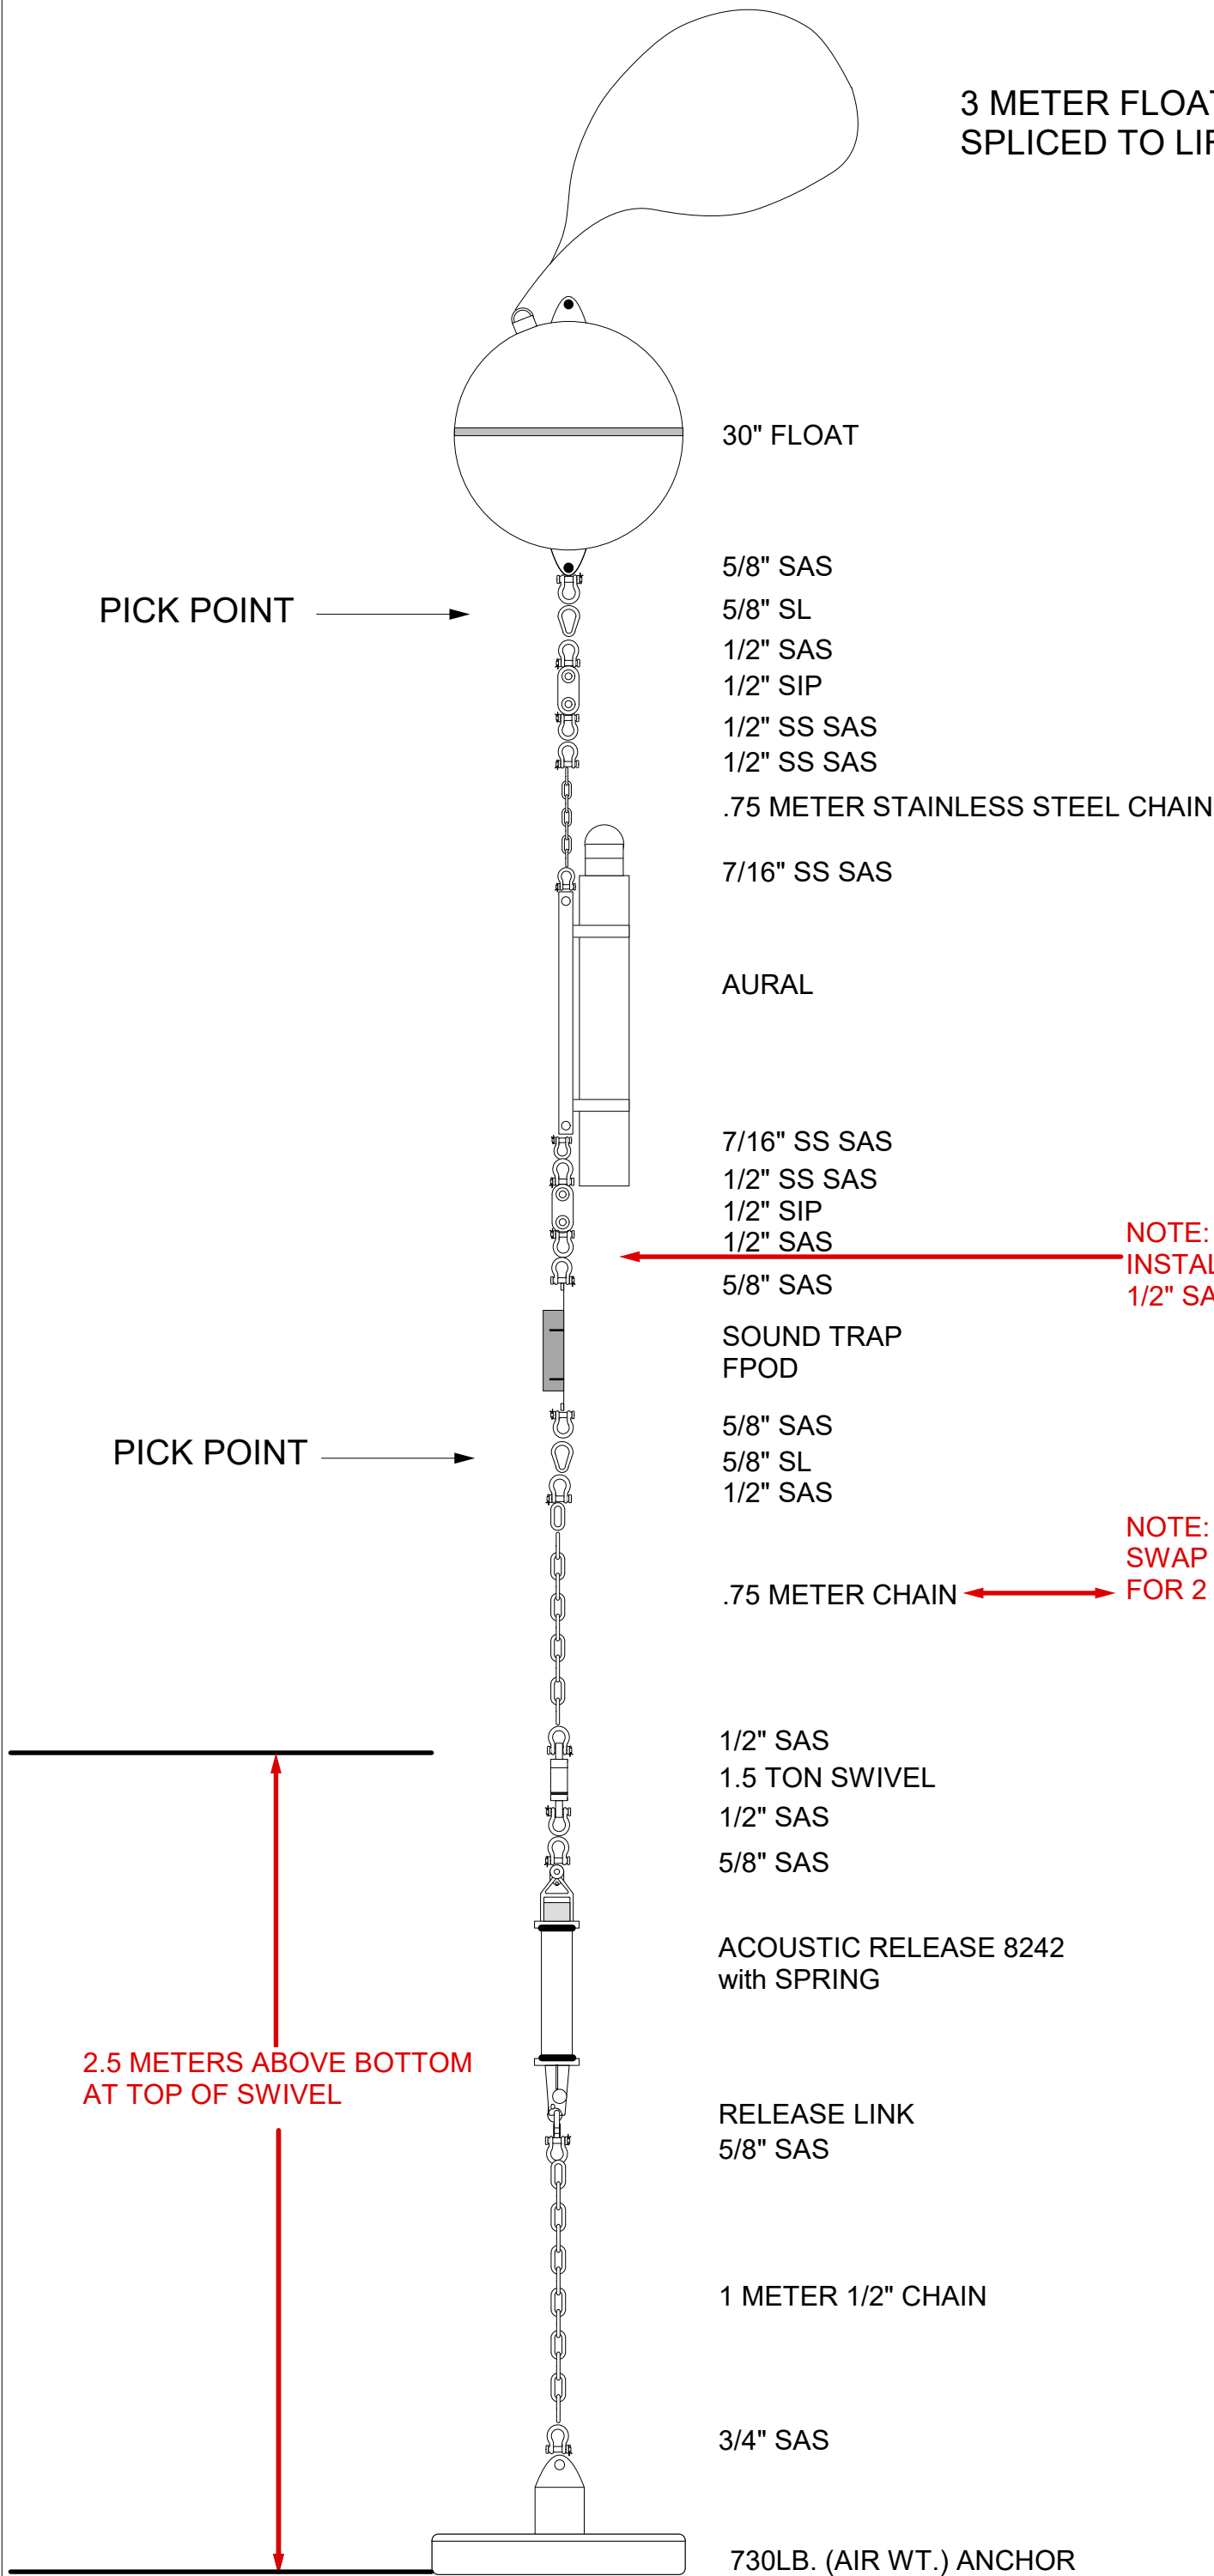

NOTE:
INSTALL 1 METER CHAIN BETWEEN
1/2" SAS FOR 2 PICK DEPLOYMENT

NOTE:
SWAP IN 2.5 METER CHAIN HERE
FOR 2 PICK DEPLOYMENT OPTION

MOORING SHOP NOTE:
ADD 1 METER AND 2.5 METER
CHAIN PER MOORING

KEY:	
SAS, SAFETY ANCHOR SHACKLE with cotter pin	
SS SAS, STAINLESS STEEL SAFETY ANCHOR SHACKLE with cotter pin	
SL, SLING LINK	
SIP, SHACKLE ISOLATOR PLATE	
 NOAA-PMEL 7600 Sandpoint Way NE Seattle, Wa. 98115 (206) 526-6023	
AURAL W/ONE CAGE	
LOCATION: BEAUFORT, BERING, CHUKCHI	
DRAWN BY: Mike Craig	DATE: 14 APRIL 2025
APPROVED BY:	DATE: