


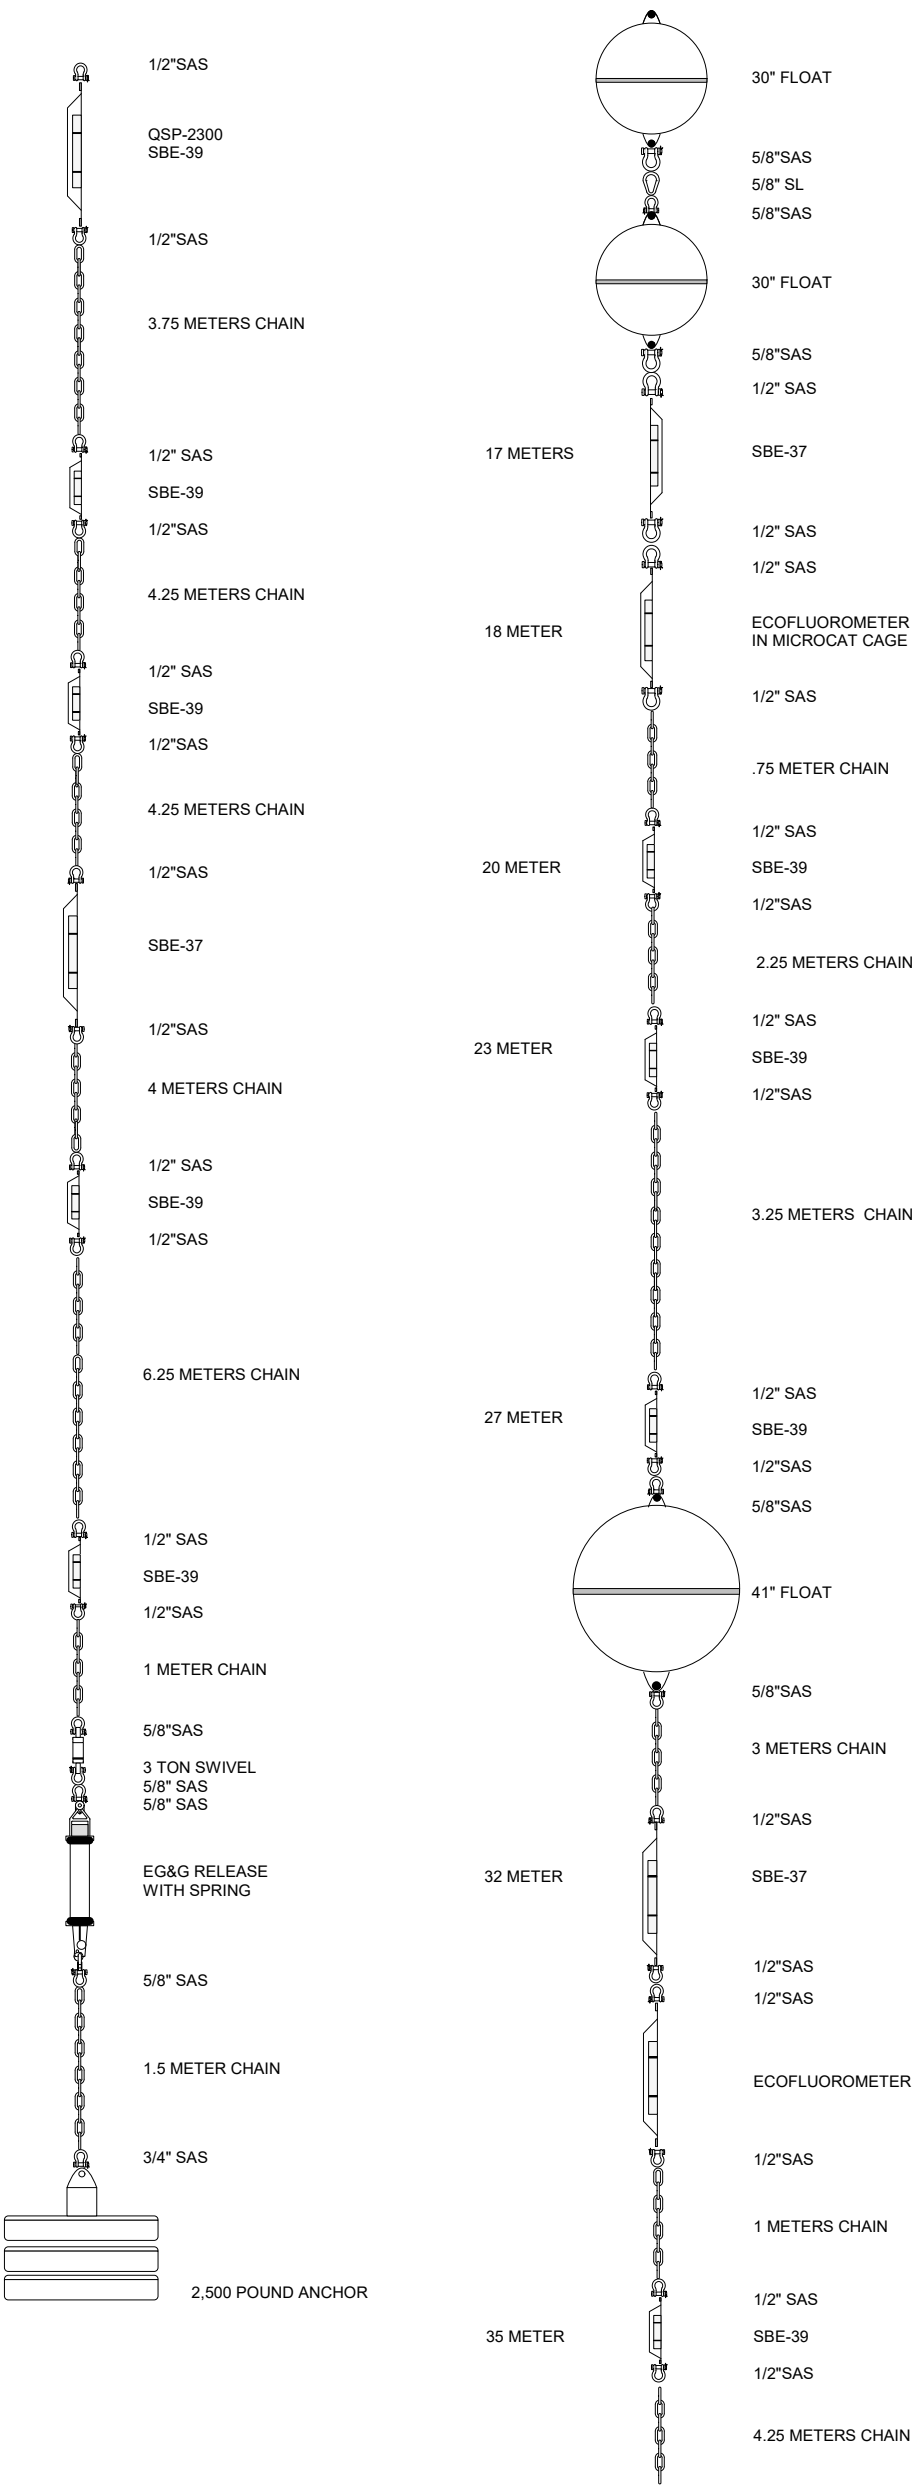

SUBSURFACE INSTRUMENTS		
DEPTH	INST.	SER #
17	SBE-37	
18	ECOFLUOR	
20	SBE-39	
23	SBE-39	
27	SBE-39	
32	SBE-37	
33	ECOFLUOR	
35	SBE-39	
40	SBE-39	
45	SBE-39	
50	SBE-39	
55	SBE-37	
60	SBE-39	
67	SBE-39	
71	BOTTOM	



NOAA-PMEL-FOCI

7600 Sandpoint Way NE
Seattle, Wa. 98115
(206) 526-6175

MOORING:	25BS-5A		
LOCATION:	BERING SEA, SITE 5		
DRAWN BY:	MIKE CRAIG	DATE:	2 JUNE 2025
APPROVED BY:		DATE:	