


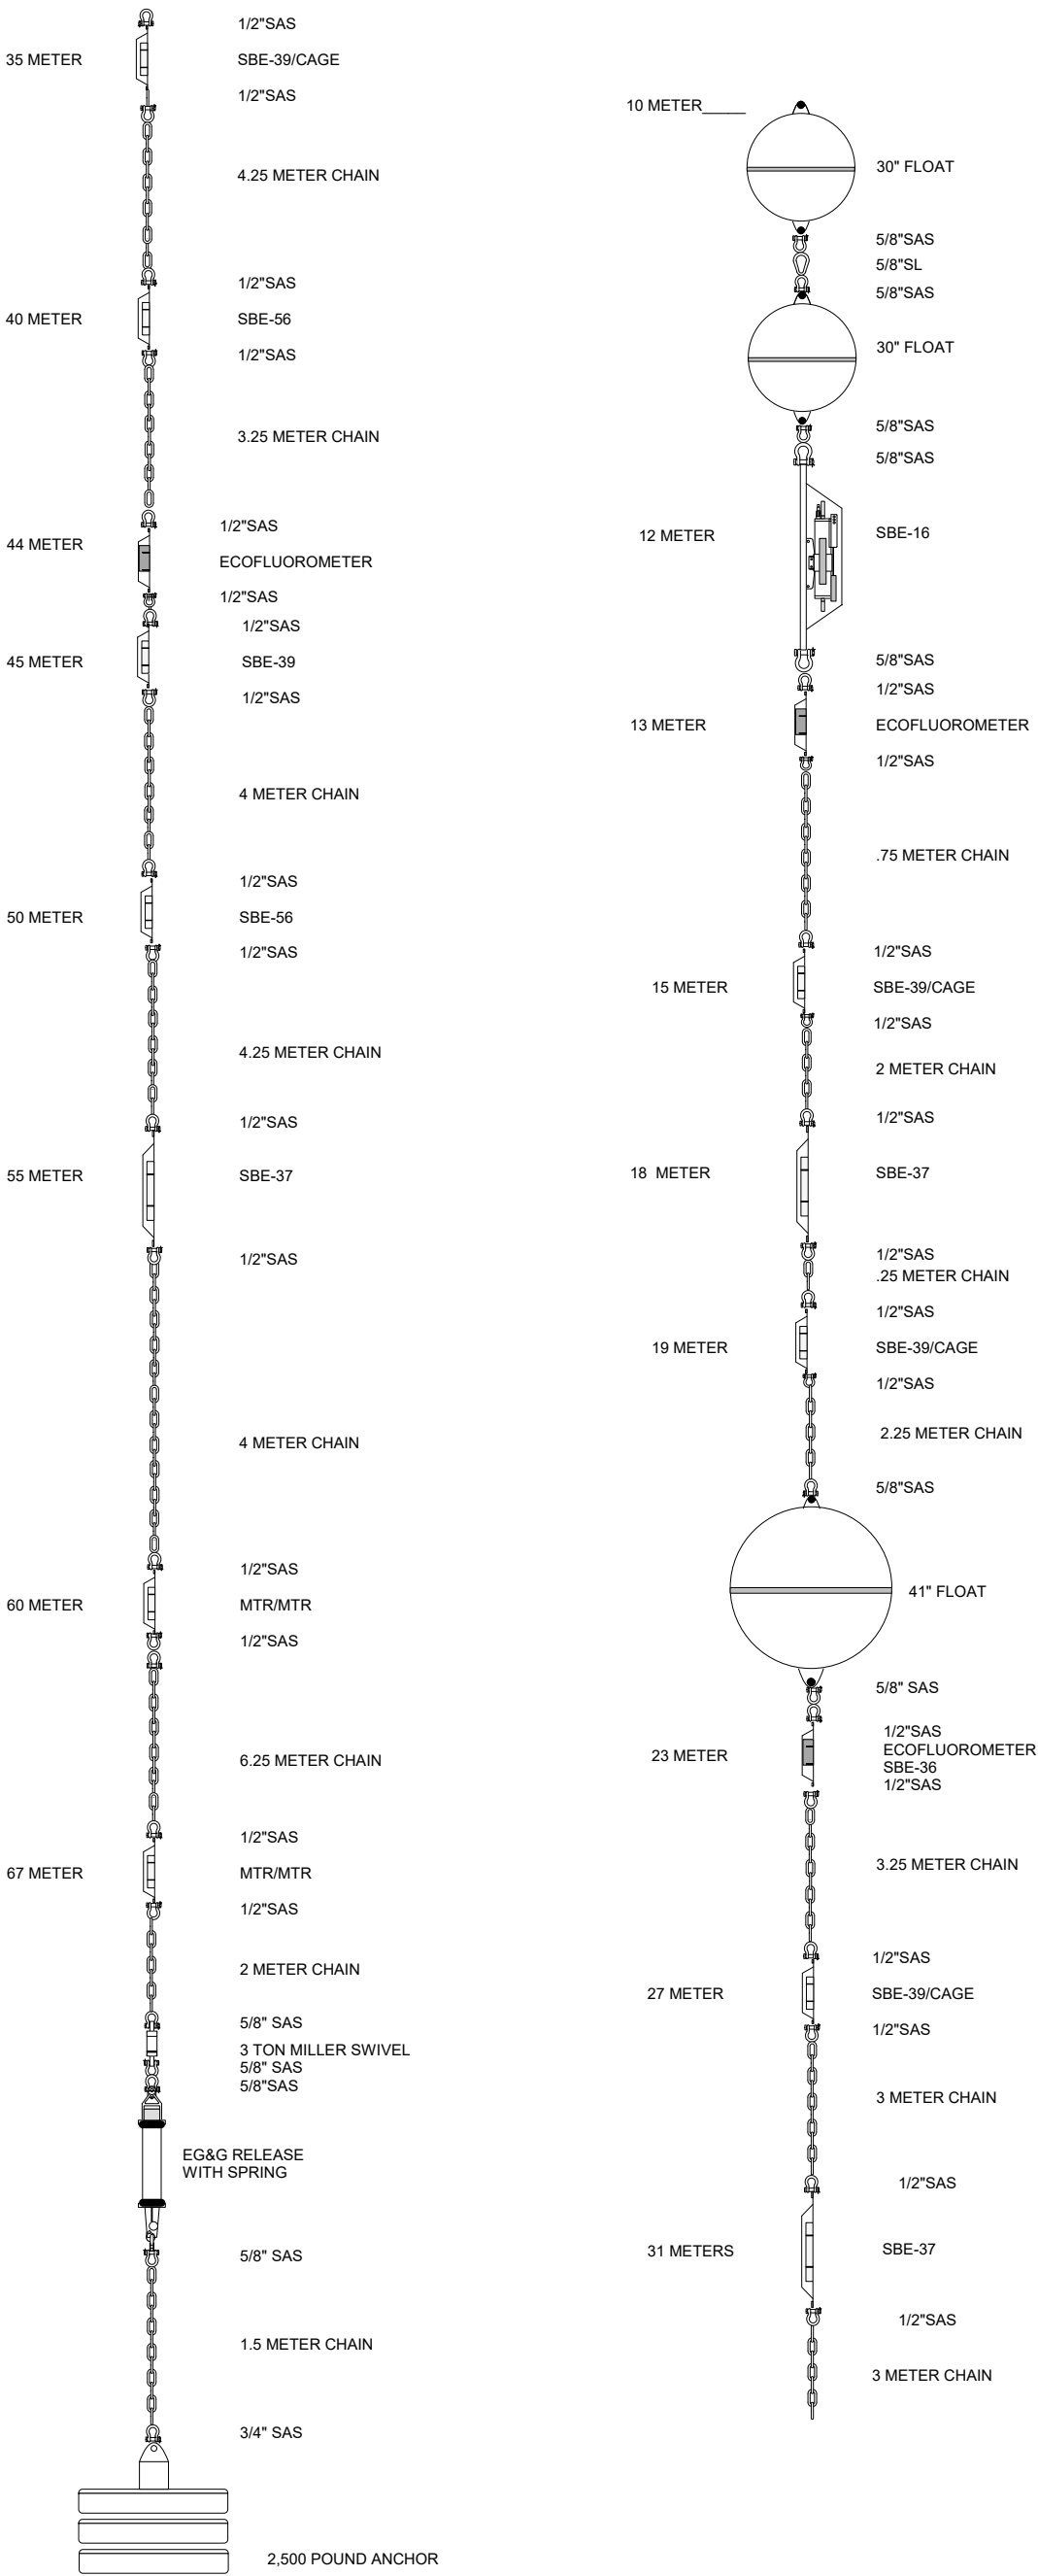

SUBSURFACE INSTRUMENTS		
DEPTH (M)	INST.	SER #
12	SBE-16	
13	ECO-FLUOR	
15	SBE-39	
18	SBE-37	
19	SBE-39	
23	SBE-36	
23	ECO-FLUOR	
27	SBE-39	
31	SBE-37	
35	SBE-39	
40	SBE-56	
44	ECO-FLUOR	
45	SBE-39	
50	SBE-56	
55	SBE-37	
60	MTR/MTR	
67	MTR/MTR	
72	BOTTOM	
 NOAA-PMEL-FOCI 7600 Sandpoint Way NE Seattle, Wa. 98115 (206) 526-6175		
MOORING: 26BS-4A		
LOCATION: BERING SEA, SITE 4		
DESIGN BY: MIKE CRAIG	DATE : 21 JANUARY 2026	
DRAWN BY:	DATE :	