


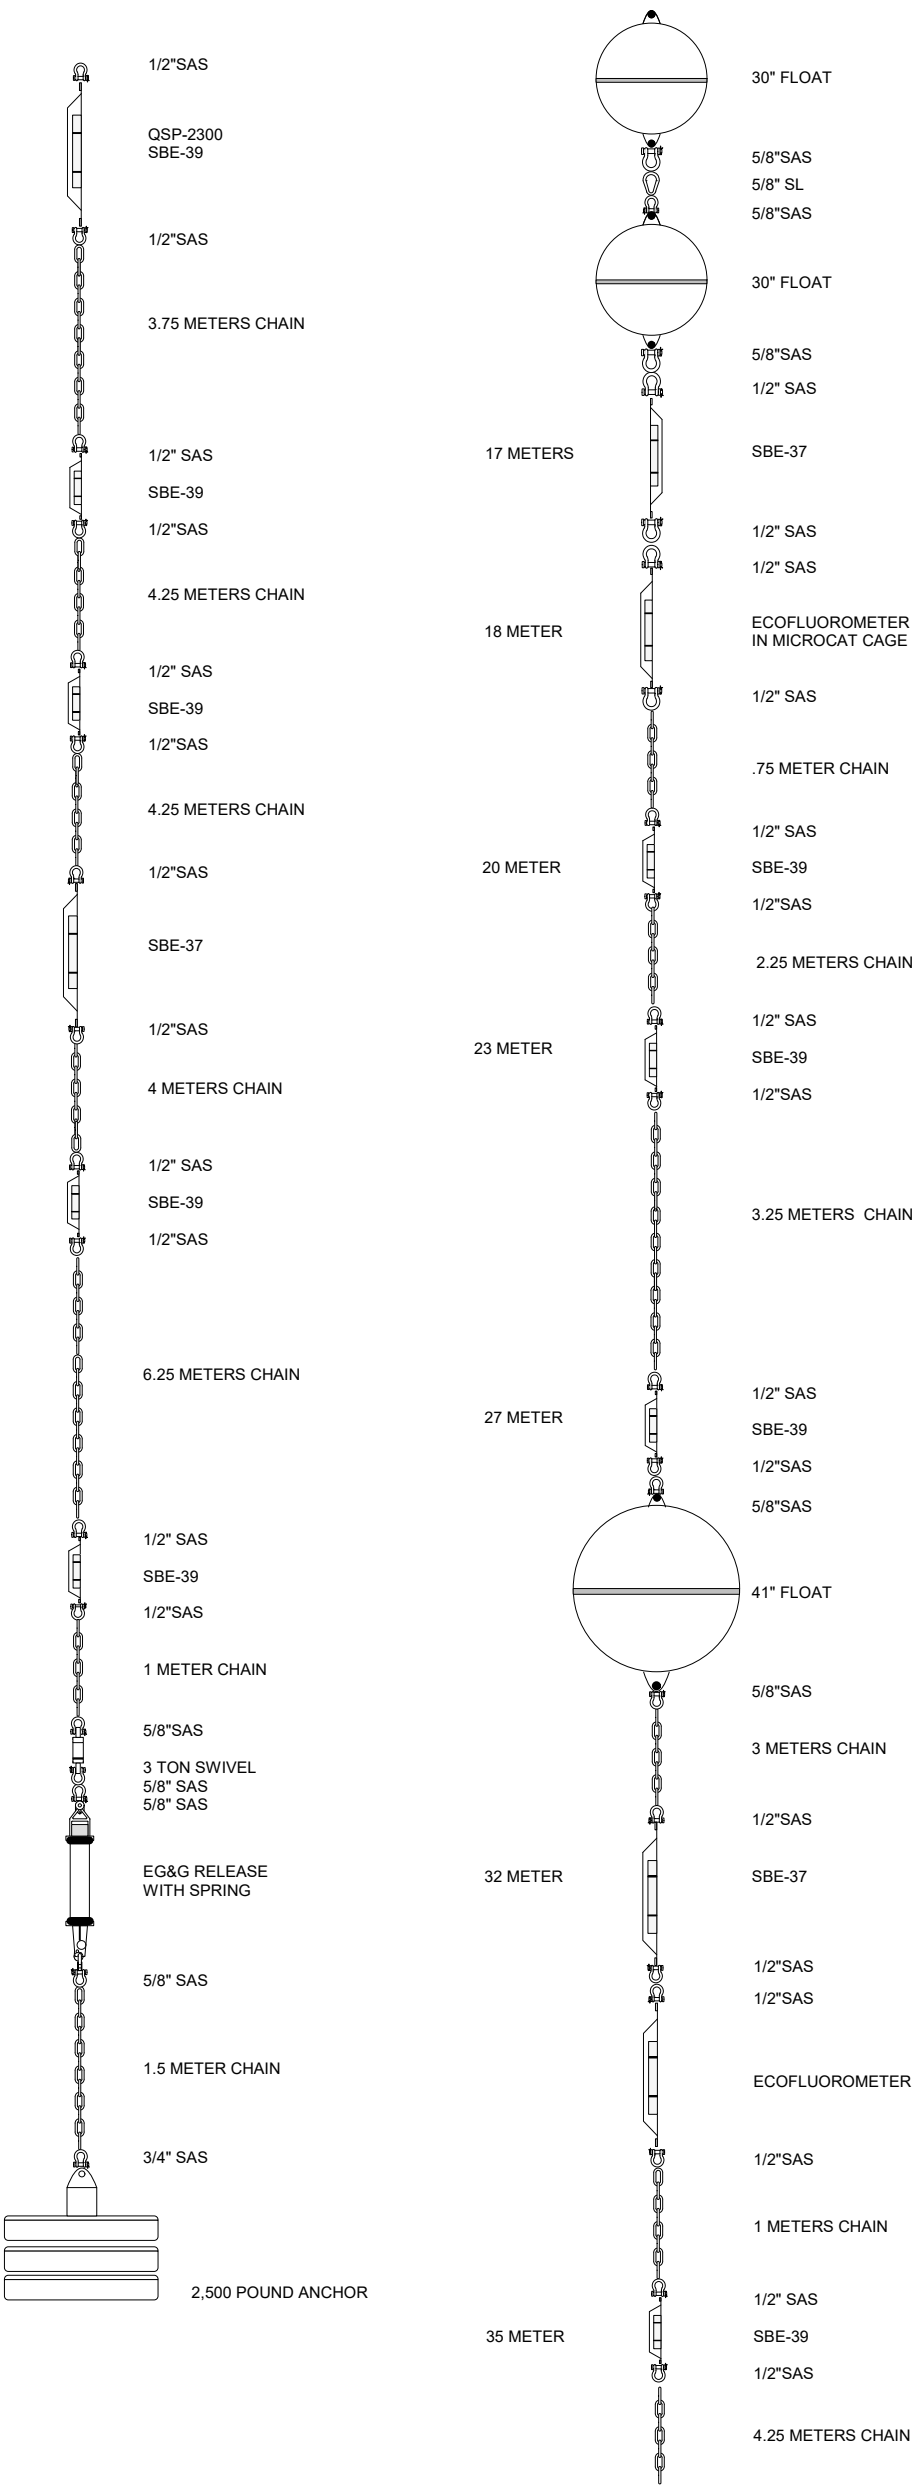

| SUBSURFACE INSTRUMENTS |          |       |
|------------------------|----------|-------|
| DEPTH                  | INST.    | SER # |
| 17                     | SBE-37   |       |
| 18                     | ECOFLUOR |       |
| 20                     | SBE-39   |       |
| 23                     | SBE-39   |       |
| 27                     | SBE-39   |       |
| 32                     | SBE-37   |       |
| 33                     | ECOFLUOR |       |
| 35                     | SBE-39   |       |
| 40                     | SBE-39   |       |
| 45                     | SBE-39   |       |
| 50                     | SBE-39   |       |
| 55                     | SBE-37   |       |
| 60                     | SBE-39   |       |
| 67                     | SBE-39   |       |
| 71                     | BOTTOM   |       |

|                                                                                       |                                                                                        |                                 |
|---------------------------------------------------------------------------------------|----------------------------------------------------------------------------------------|---------------------------------|
|  | <b>NOAA-PMEL-FOCI</b><br>7600 Sandpoint Way NE<br>Seattle, Wa. 98115<br>(206) 526-6175 |                                 |
|                                                                                       | <b>MOORING:</b><br>26BS-5A                                                             |                                 |
| <b>LOCATION:</b><br>BERING SEA, SITE 5                                                |                                                                                        |                                 |
| <b>DRAWN BY:</b><br>MIKE CRAIG                                                        |                                                                                        | <b>DATE:</b><br>21 JANUARY 2026 |
| <b>APPROVED BY:</b>                                                                   |                                                                                        | <b>DATE:</b>                    |